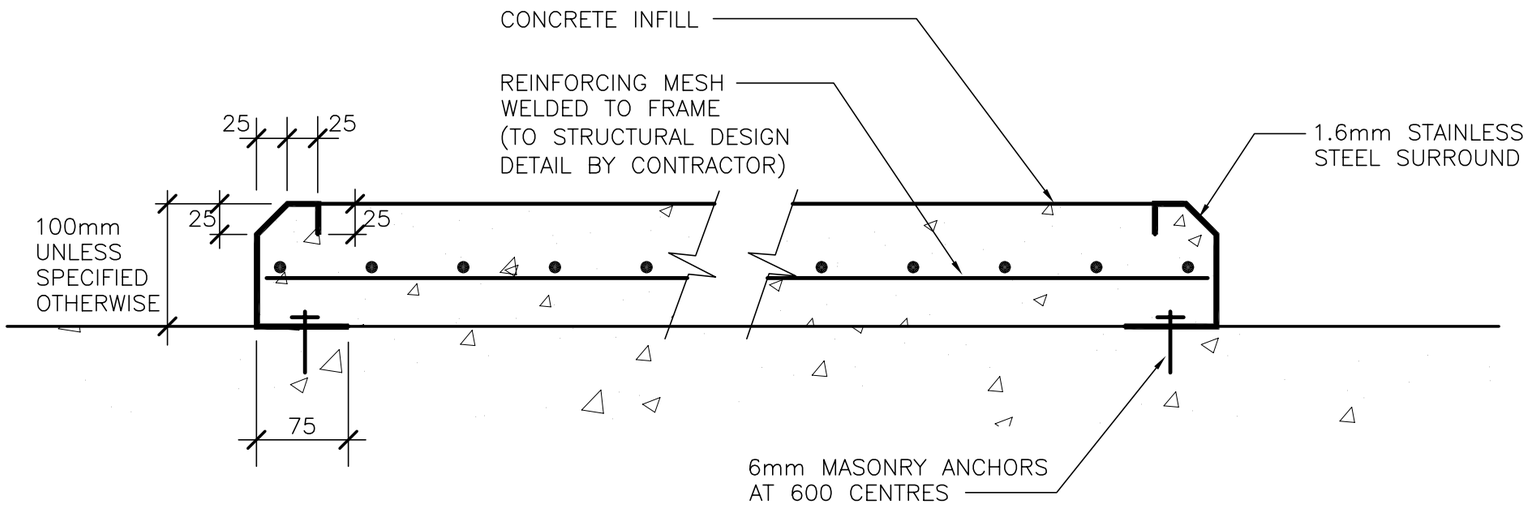

A	PRELIMINARY	A.S.	23/04/2018
REV.	REVISION DESCRIPTION		DATE

AWP PROJECTS

Title
TYPICAL GENERAL PLANT
PLINTH DETAIL

Drawn G.K. Date 23/04/2018	File AWP TITLE BLOCK.dwg
Checked Date	Approved Date
Scale N.T.S	Plotted Date 24/04/2018
Drawing Number AWP-M-05	Revision A