

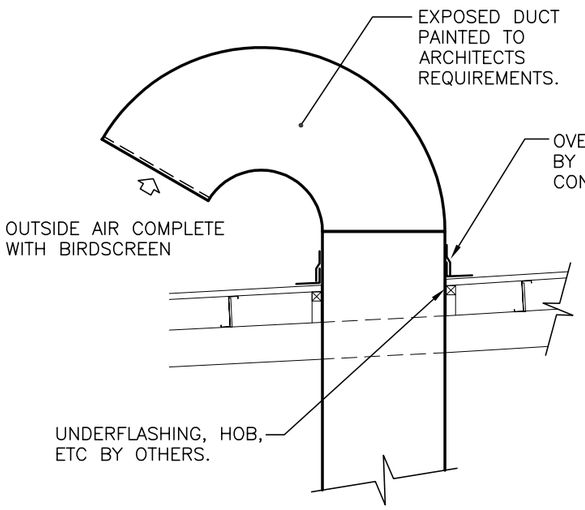


DETAIL 1: "GOOSE NECK" INTAKE

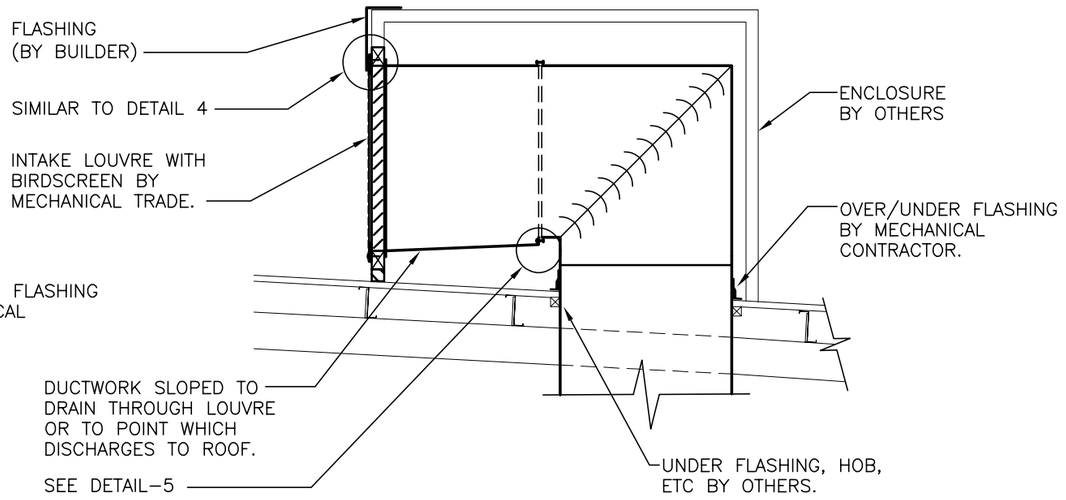


DETAIL 2: "ENCLOSED" INTAKE

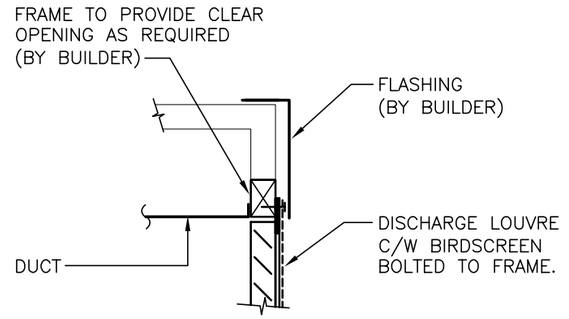


DETAIL 4



DETAIL 5

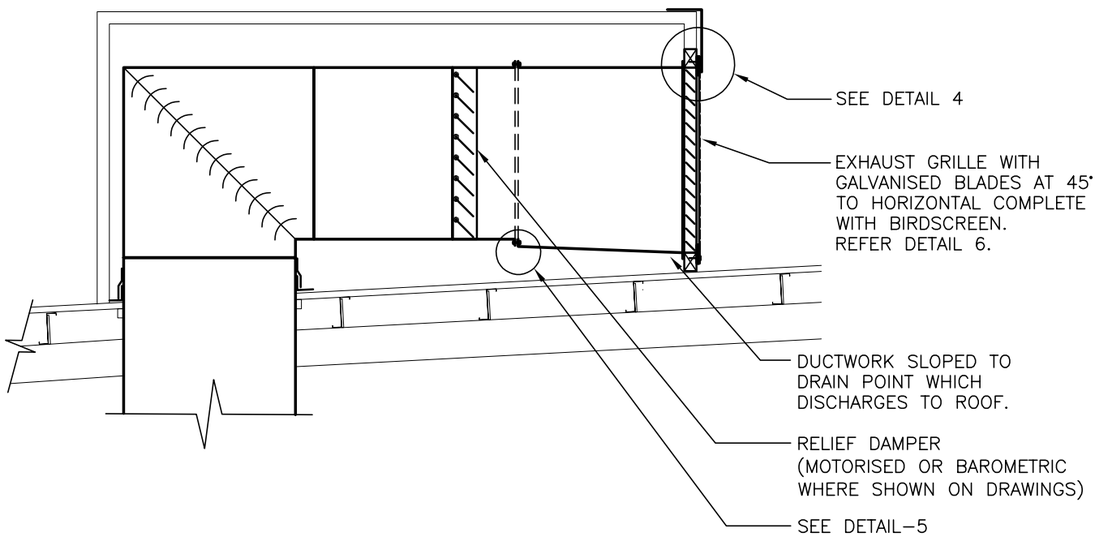

DETAIL 3: "ENCLOSED" DISCHARGE

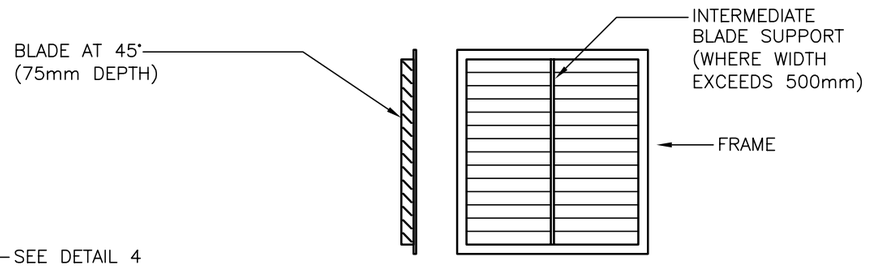

DISCHARGE LOUVRE

DETAIL 6

REV.	REVISION DESCRIPTION		DATE
A	PRELIMINARY	A.S.	23/04/2018

AWP PROJECTS

Title
ROOF MOUNTED AIR INTAKE AND DISCHARGE DETAILS

Drawn G.K.	Date 23/04/2018	File AWP TITLE BLOCK.dwg	
Checked	Date	Approved	Date
Scale N.T.S		Plotted Date 24/04/2018	
Drawing Number AWP-M-06		Revision A	